


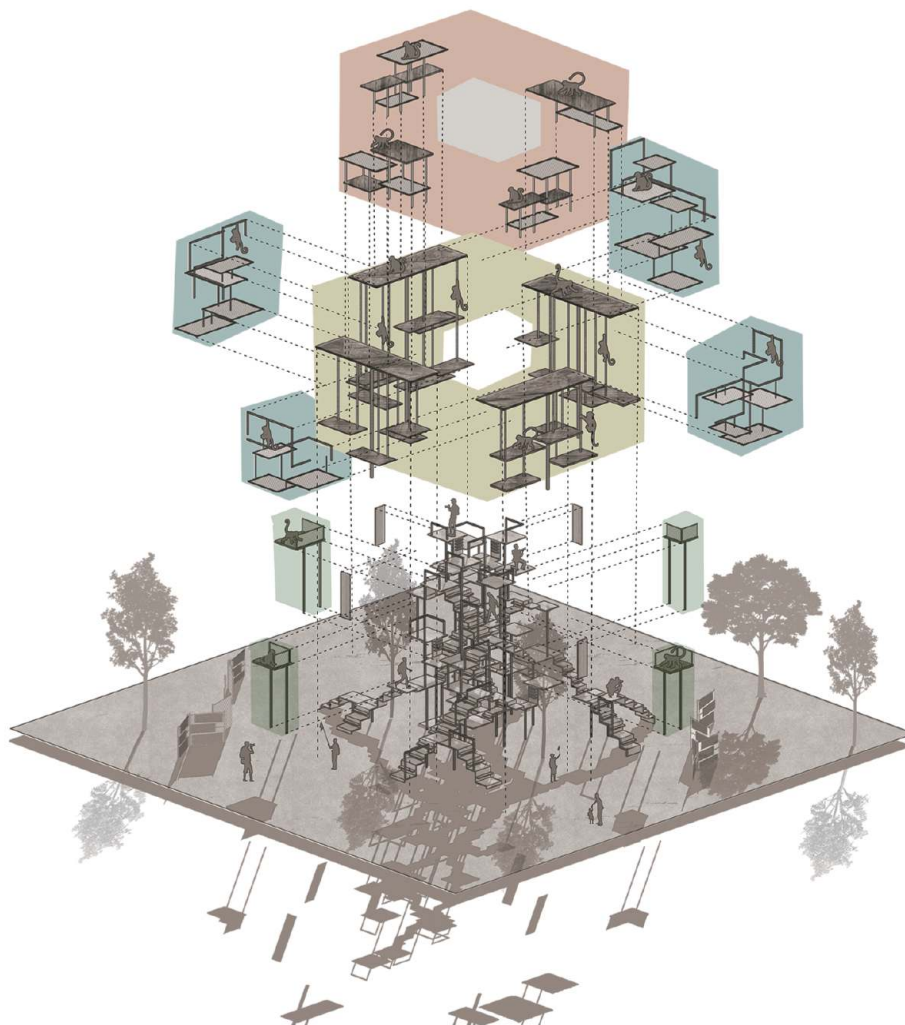

Hung Yung Fan
Architecture Portfolio

...

National Taiwan University of Science and Technology

Selected works

[2021-2023]



洪詠凡

Hung Yung Fan

2001 / 12 / 15

About me

Hello, I'm Emily Hung. I enjoy participating in various new and fresh activities, as I am always willing to step out of my comfort zone and enjoys interacting with others.

During high school, I developed a passion for campsite construction in the Scouts. I took the opportunity to create layout plans, build models, and construct public facilities in campsite using bamboo. I found the process of transforming 2D concepts into 3D structures fascinating. Even to this day, I find great joy in creating handmade models. I believe this was the catalyst that sparked my curiosity in architecture.

During my freshman year, I participated in the USR Bamboo Construction Project. I collaborated with professors to exhibit and construct bamboo structures in local areas in Chiayi. It made me realize the importance of blending and transforming the human environment with architecture in order to create designs that are human-centered. I have continued to apply this concept to every design project, and I consistently seek out new challenges in every moment since I feel a great sense of accomplishment every time I learn something new from each experience!

Contact me

Phone : 0965315111

Gmail : hungyungfan@gmail.com

Education

2020-present

National Taiwan University of Science and Technology

2018-2020

Ching Cheng High School

Language


TOIEC / 890

GEPT High-Intermediate

TOEFL ITP / 587

Advanced French course / 128hr

Software Skills

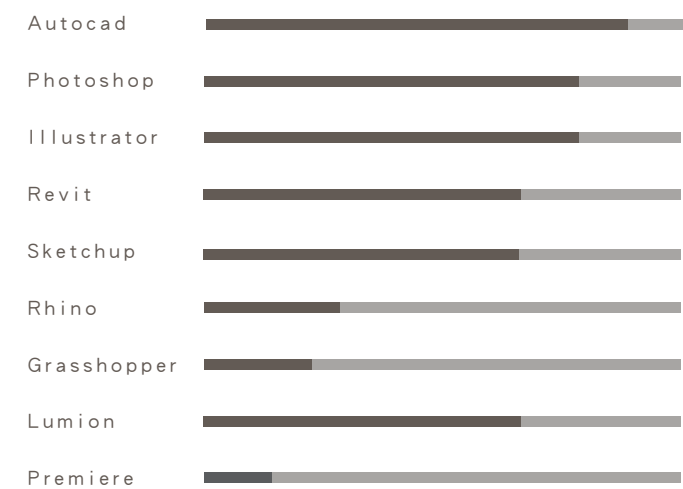

Workshop & Competition

- | | |
|------|---|
| 2023 | The National Architects Association of the Republic of China Students Contest / Selected award |
| 2022 | Bamboo Forest Iron Cenozoic Exhibition / Practical Achievement- Gold Award |
| 2022 | Training for Accessible Facilities and Equipment Design Inspection Personnel |
| 2021 | USR Bamboo Construction Project |
| 2020 | Tellus Home Design Competition / Selected award |

Experience

Internship@Bio-Architecture Formosana
[2022.07-2022.09]

Contents

01

Hybrid International Youth Hostel

02

The world is lacking an X space - Dinner Theater

03

Digital Building Fabrication Center

04

Hydrological Exhibition Center

05

Handmade Models / Sketchings

01



Hybrid International Youth Hostel


X




House

Chifeng str., a street with classic beauty near our site, which is also called 『歹鐵仔街』, I used the idea of industrial elements to create my concept, as a wrench and screw go together, I want my design to unite public, historical and local characteristics values. I hope my building to unite this characteristics and pull them closer for the hostel guests to experience them deeply.

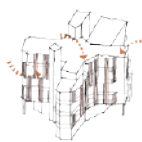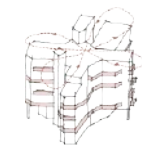

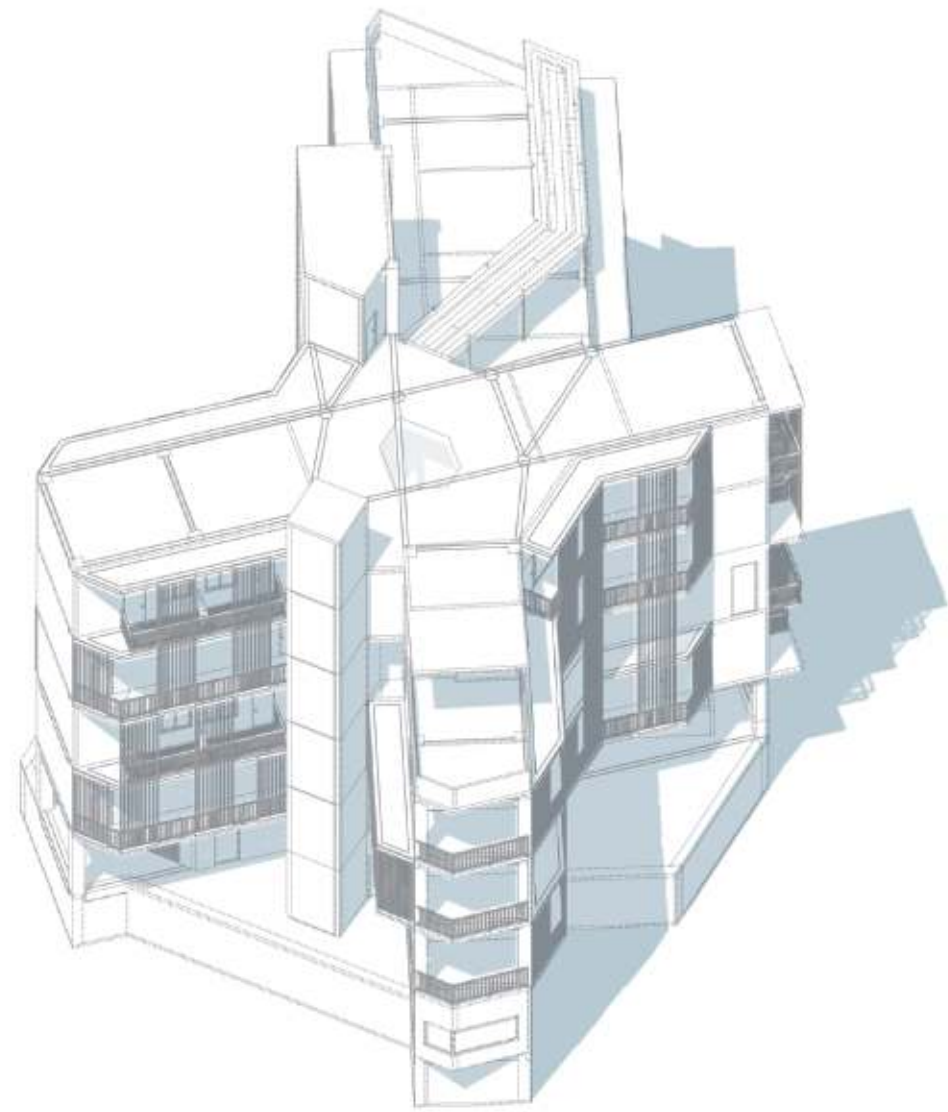


Massing development

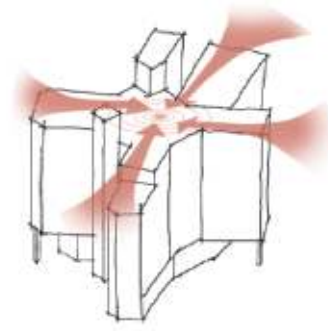


X-shaped geometry

- Generates a connective central space
- Circulation keeps diverging & converging

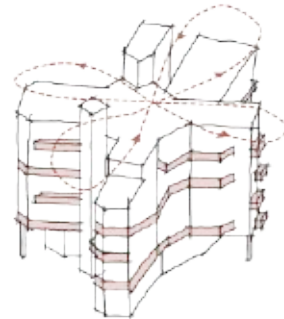

Balcony and corridor staggering

- Build up traffic flow between each space
- Allow wind and sunlight inside the building

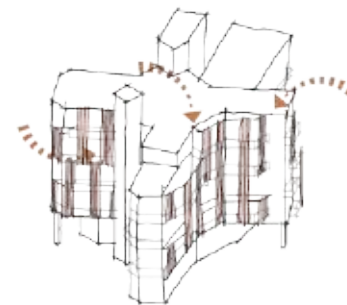

Semi-outdoor corridor

- Add second skin to protect privacy and prevent some heat from entering the building

Site analysis



Traffic analysis


- Songshan-Xindian Line
- Tamsui-Xinyi Line
- Linear park
- Public Bicycle System
- Zhongshan, Shuanglian Station
- Zhongshan Station
- Bus stop




Hostel distribution

- Hostel
 - Hostel offer breakfast
- 17%


Concept

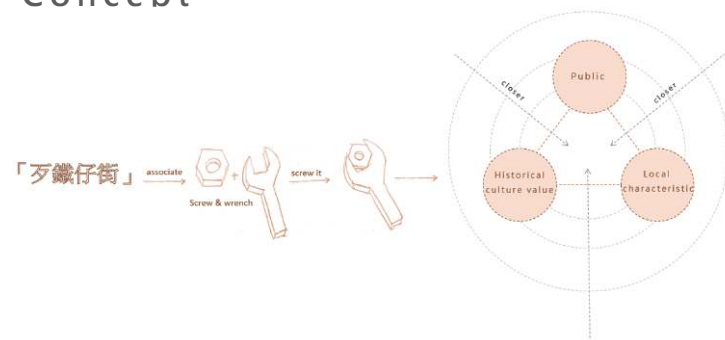

Associate it as screw & wrench and screw it !
Be closer to public, historical culture value,
local characteristic

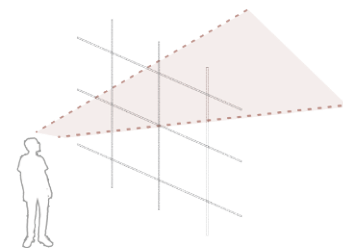


Transparent & Light

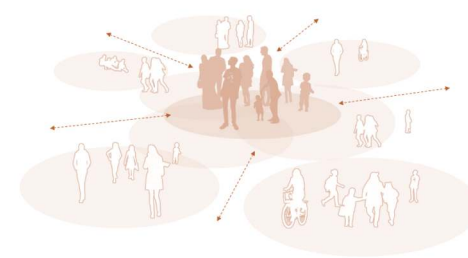


Converge & Diverge


Site plan

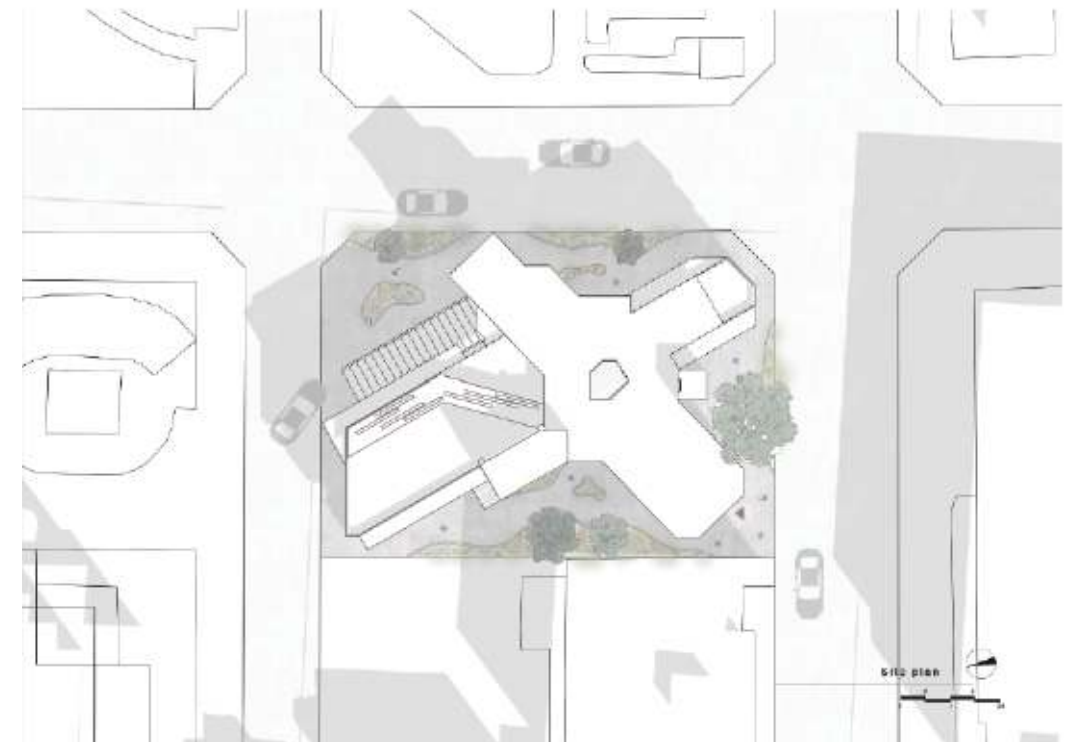

Floor plan

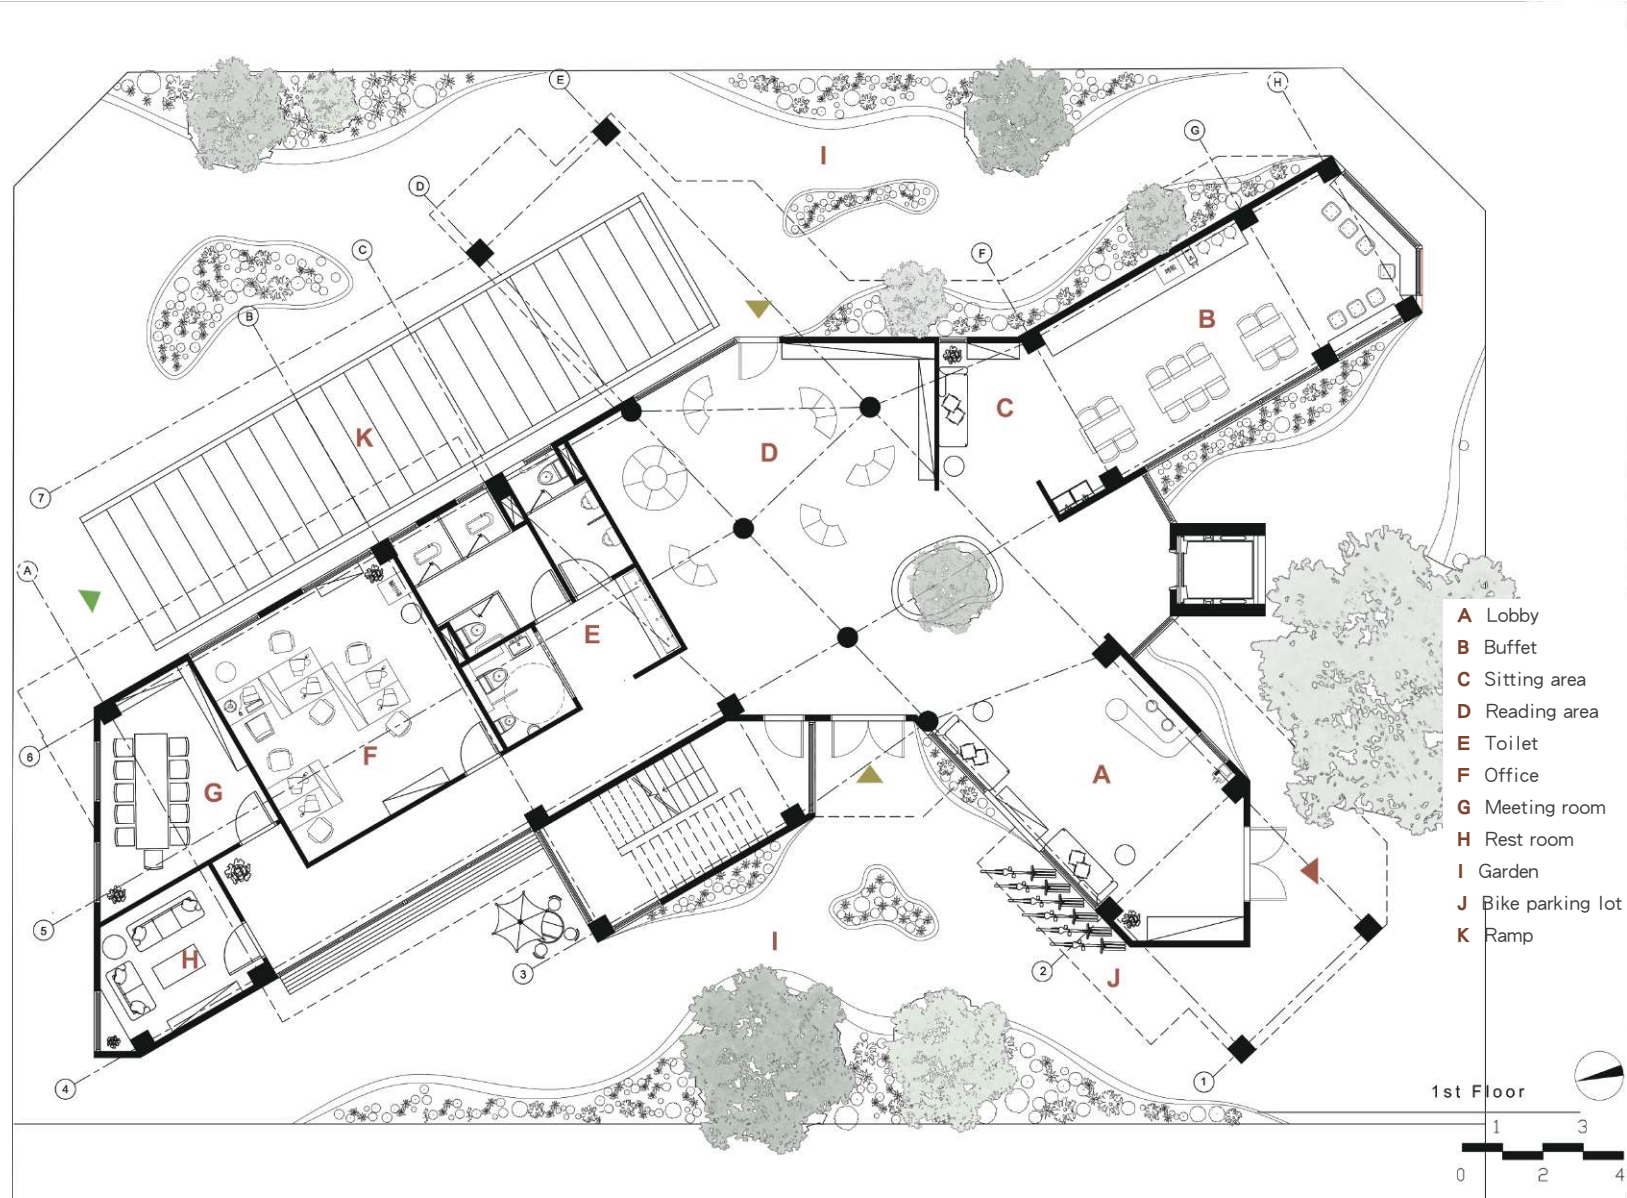

Section

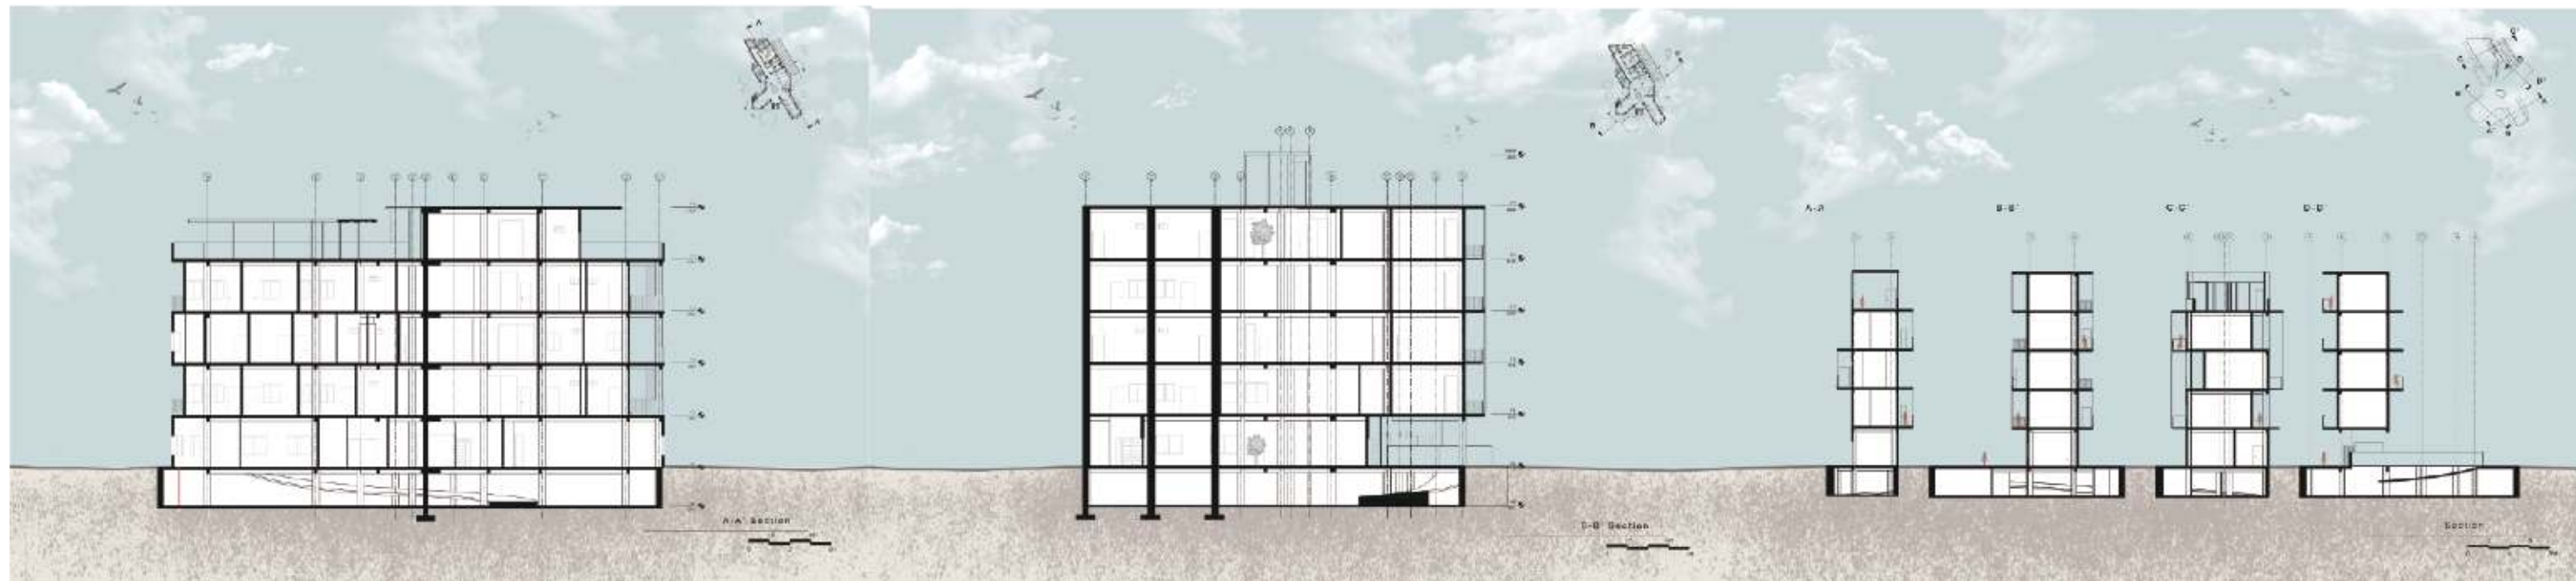




Rendering



Elevation



Floor plan

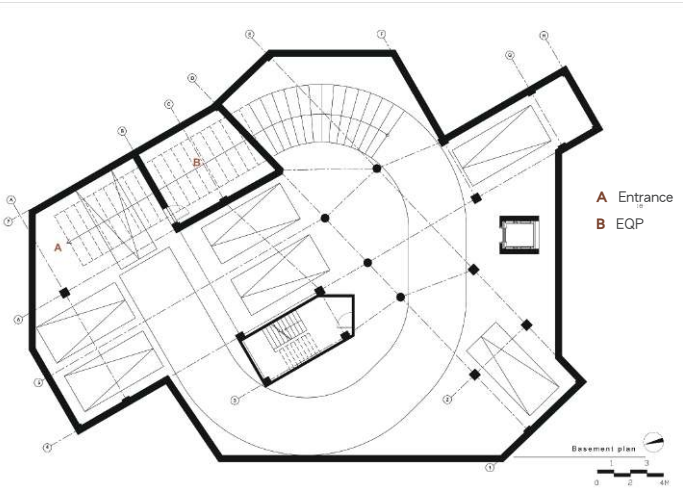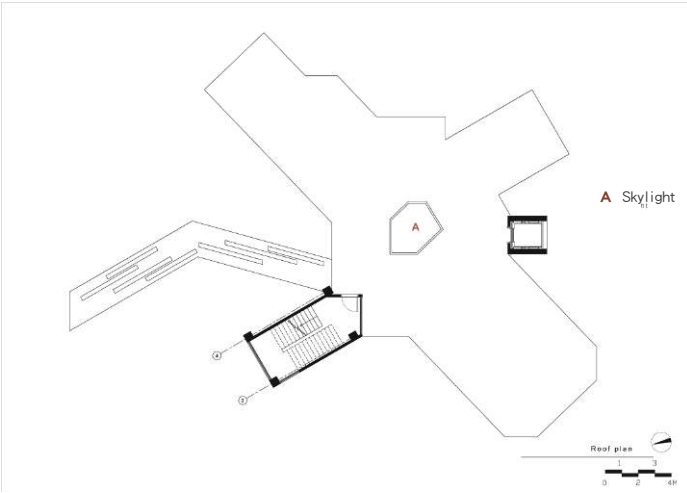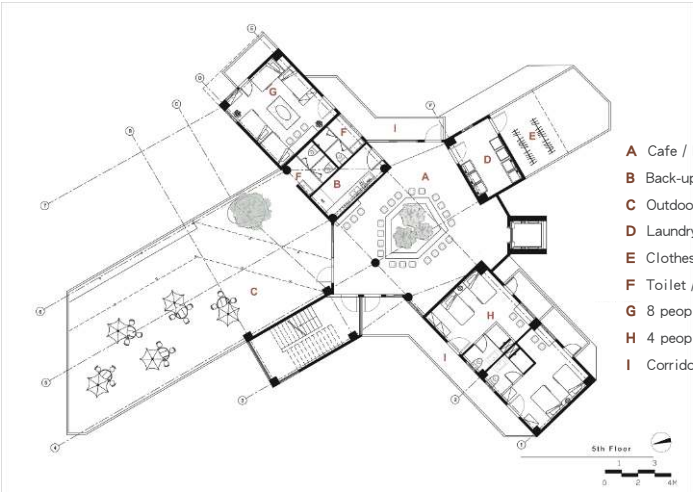


Room plan




- ① Bunk bed x 1
- ② Bathroom
- ③ Share area
- ④ Desk
- ⑤ Locker

Double room

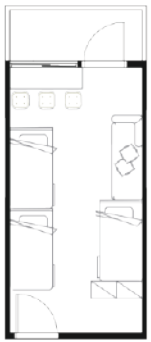


6 people room

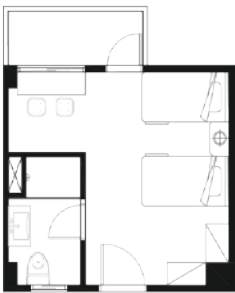

- ① Bunk bed x 2
- ② Bathroom
- ③ Balcony
- ④ Desk
- ⑤ Locker

4 people room

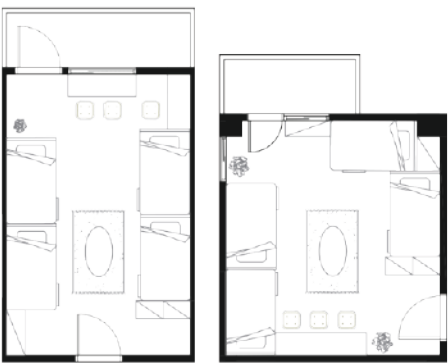

8 people room

- ① Bunk bed x 4
- ② Balcony
- ③ Desk
- ④ Locker

Outdoor rendering




02

The world is lacking an X space - Dinner Theater


聲波煮場秀

In this design, the site will be defined as a complex space consisting of a music square, restaurants, and theaters. Through the "sonic seasoning" method, music and food will be fused together, allowing the public to experience the space in rich and diverse forms. This space will extend the leisurely pace of life in Taichung and integrate the food culture of breweries and Taichung's market. It will also enhance the dining functions within the park, using food, music, and performances to interact and season, creating an interface space for the four surrounding areas of the site. At last, we hope to generate resonance that stimulates all five senses, and enjoying the perfect harmony of music and cuisine in the right rhythm, melody, and space.

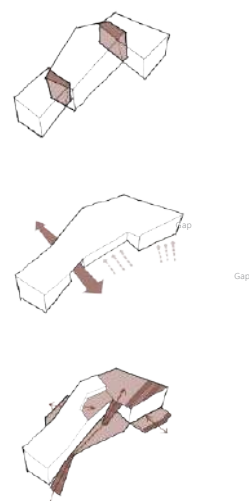




About X space

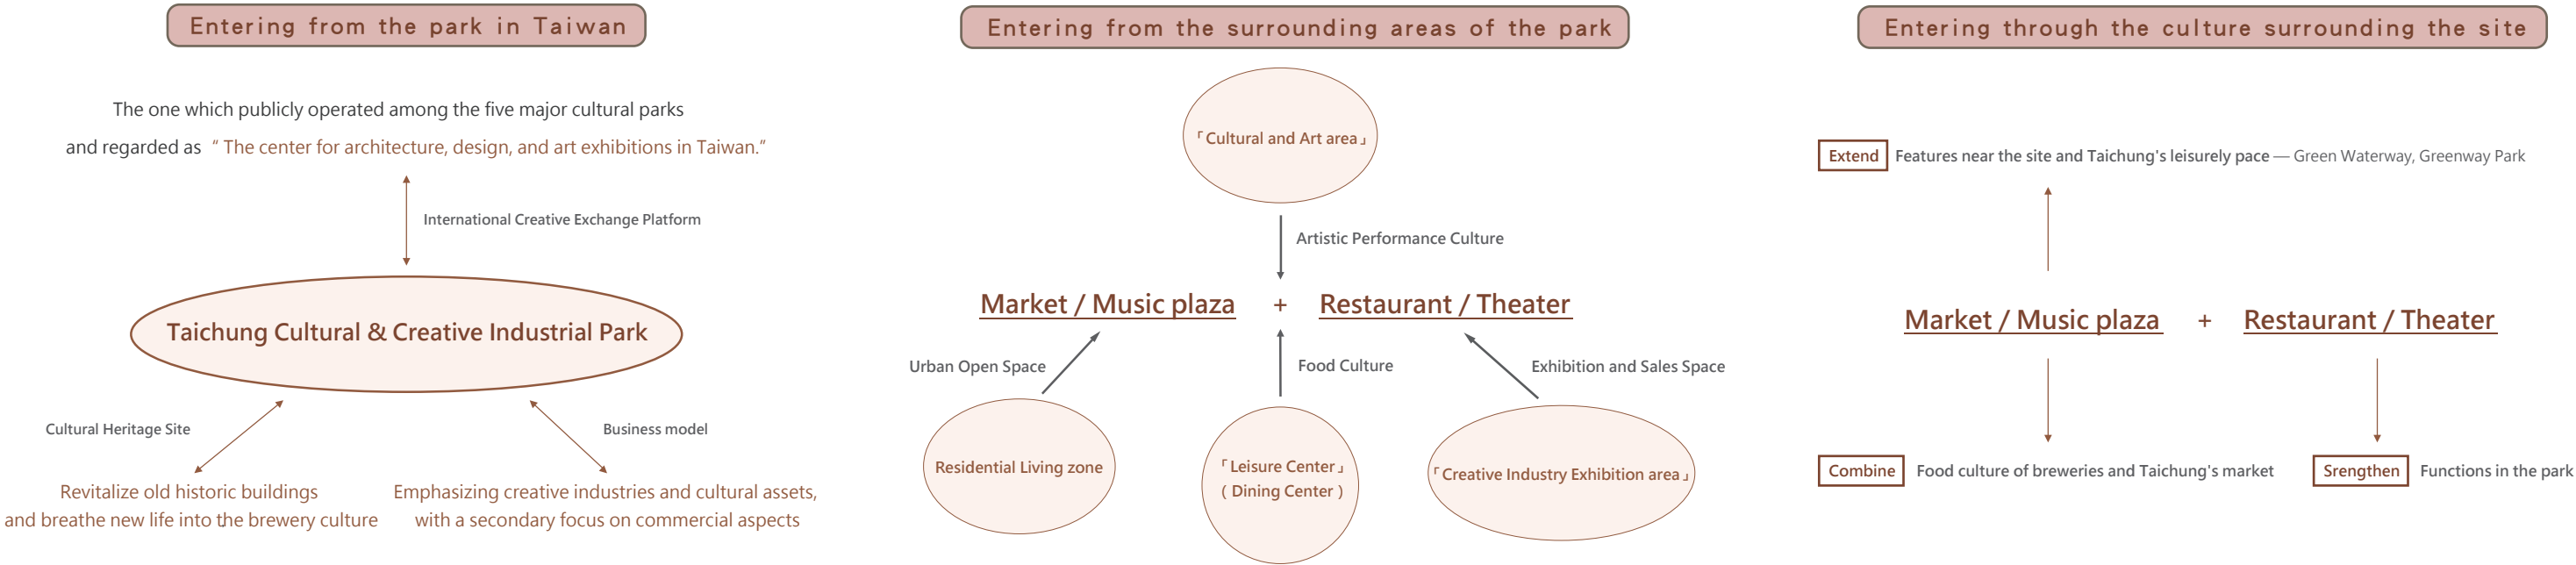


Concept




Fuction

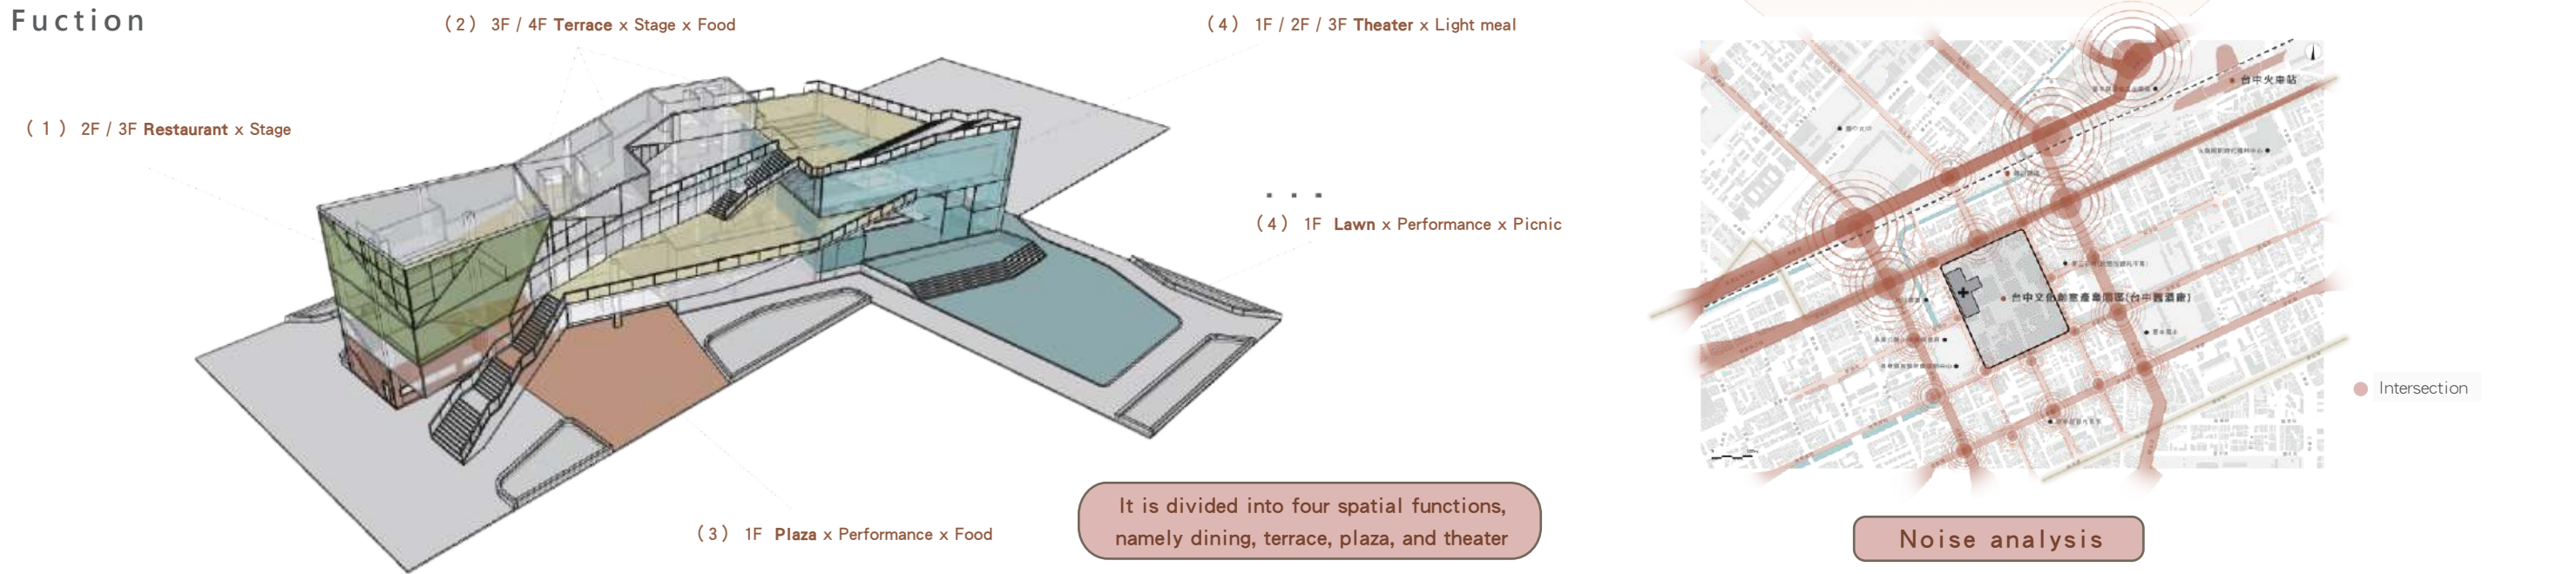

Massing development

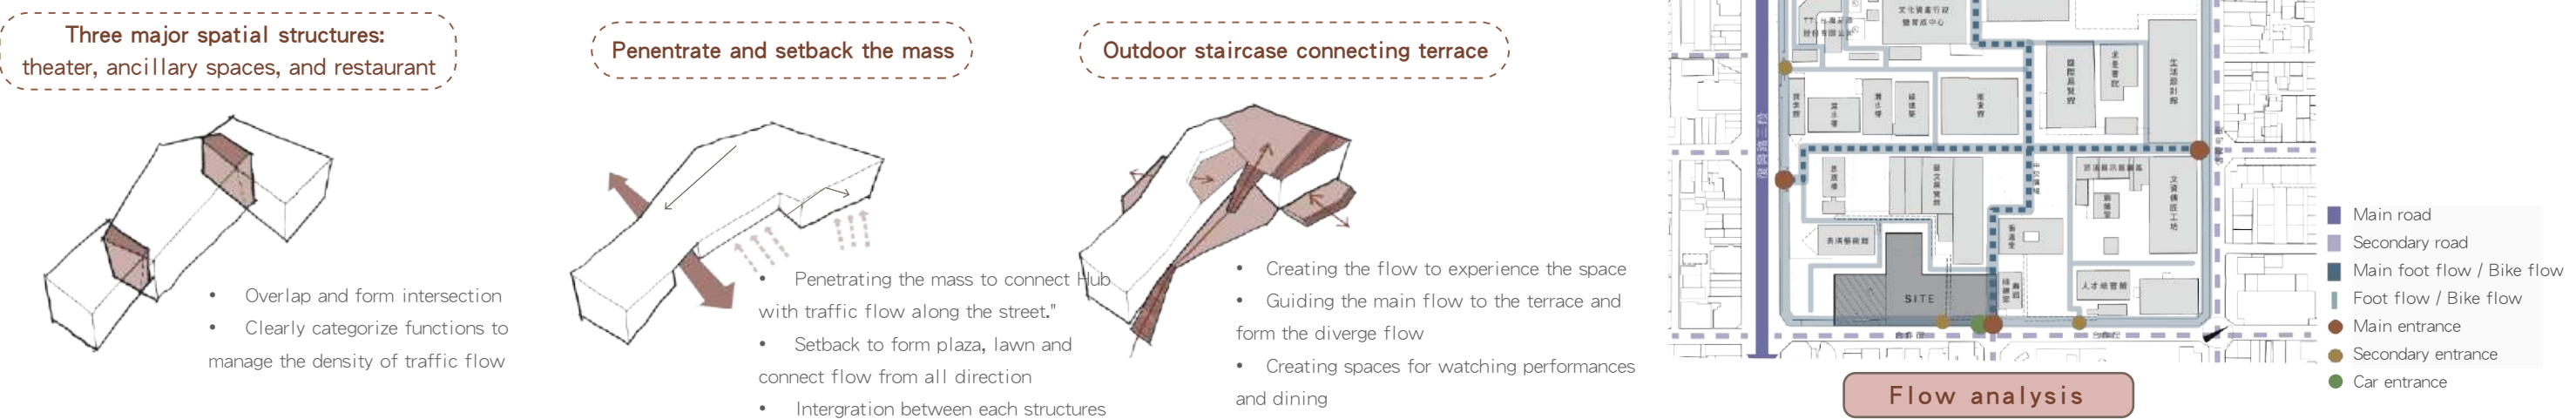

Site plan

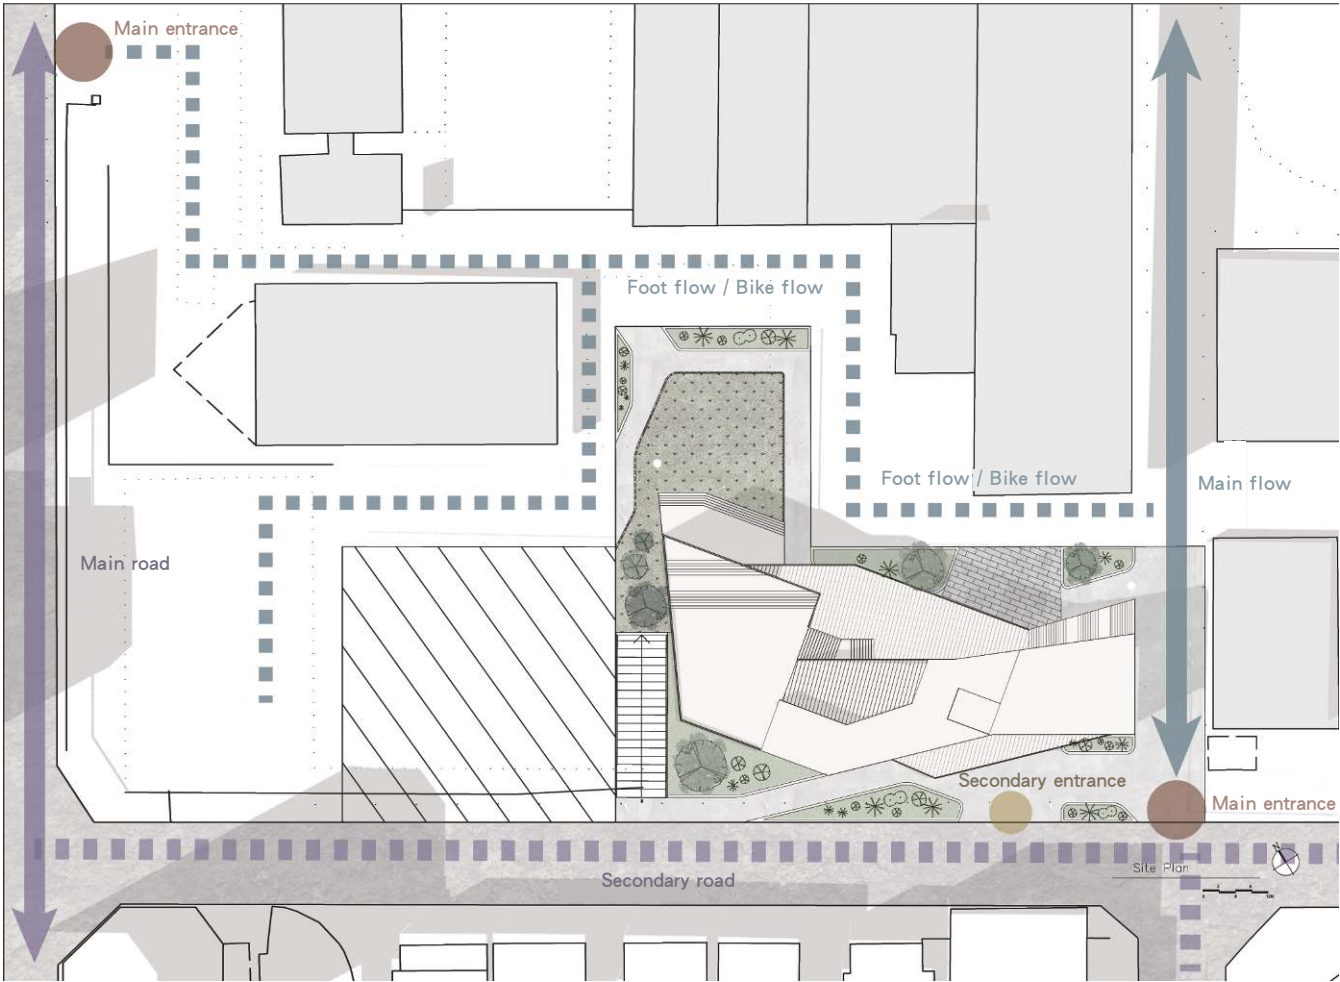

Sound1 1F Open Air Theater

- Activity : Picnic / Open air bar / Holiday market / Music festival
- Feature :
- Ideal for good weather in Taichung
 - Triple interaction, highly flexible space (internally, externally, and towards the plaza)
 - Plaza shaped by the intersection of the flow
 - The main building isolates the urban sounds from the street
 - It can be connected with the cultural and art area in the future



Sound 2 1-3F Inside the theater

- Activity : Comfortable seating and individual dining table / Opening theater
- Feature :
- The stage forms interface space between the interior and exterior, and the opening range can also be determined based on the performance format
 - Performance can extend to seating areas or lawn beyond the stage
 - Create a unique and comfortable experience different from conventional theaters



Sound 3 1F Plaza

- Activity : It serves as a dining space for takeout customers. Guests can also sit on along the flowerbed, enjoying their meal while watching performances under Hub or beside the lawn.
- Feature :
- Guide and gather the flow
 - Two-way viewing plaza



Sound 4 2-3F Dinner theater


- Activity : Enjoying performances while dining in the restaurant
- Feature :
- Providing completed dining function just like a restaurant
 - Divided into upper and lower levels for viewing performances
 - Skylights above the stage area create natural stage lighting during the day
 - All seats are designed to face towards the stage





Sound 4 3F Terrace

- Activity : Enjoying performances under Hub and on the lawn on the terrace (with bar tables and sitting area along the edge of terrace)
- Feature :
- Guide and gather the flow
 - Two-way viewing plaza


Floor plan

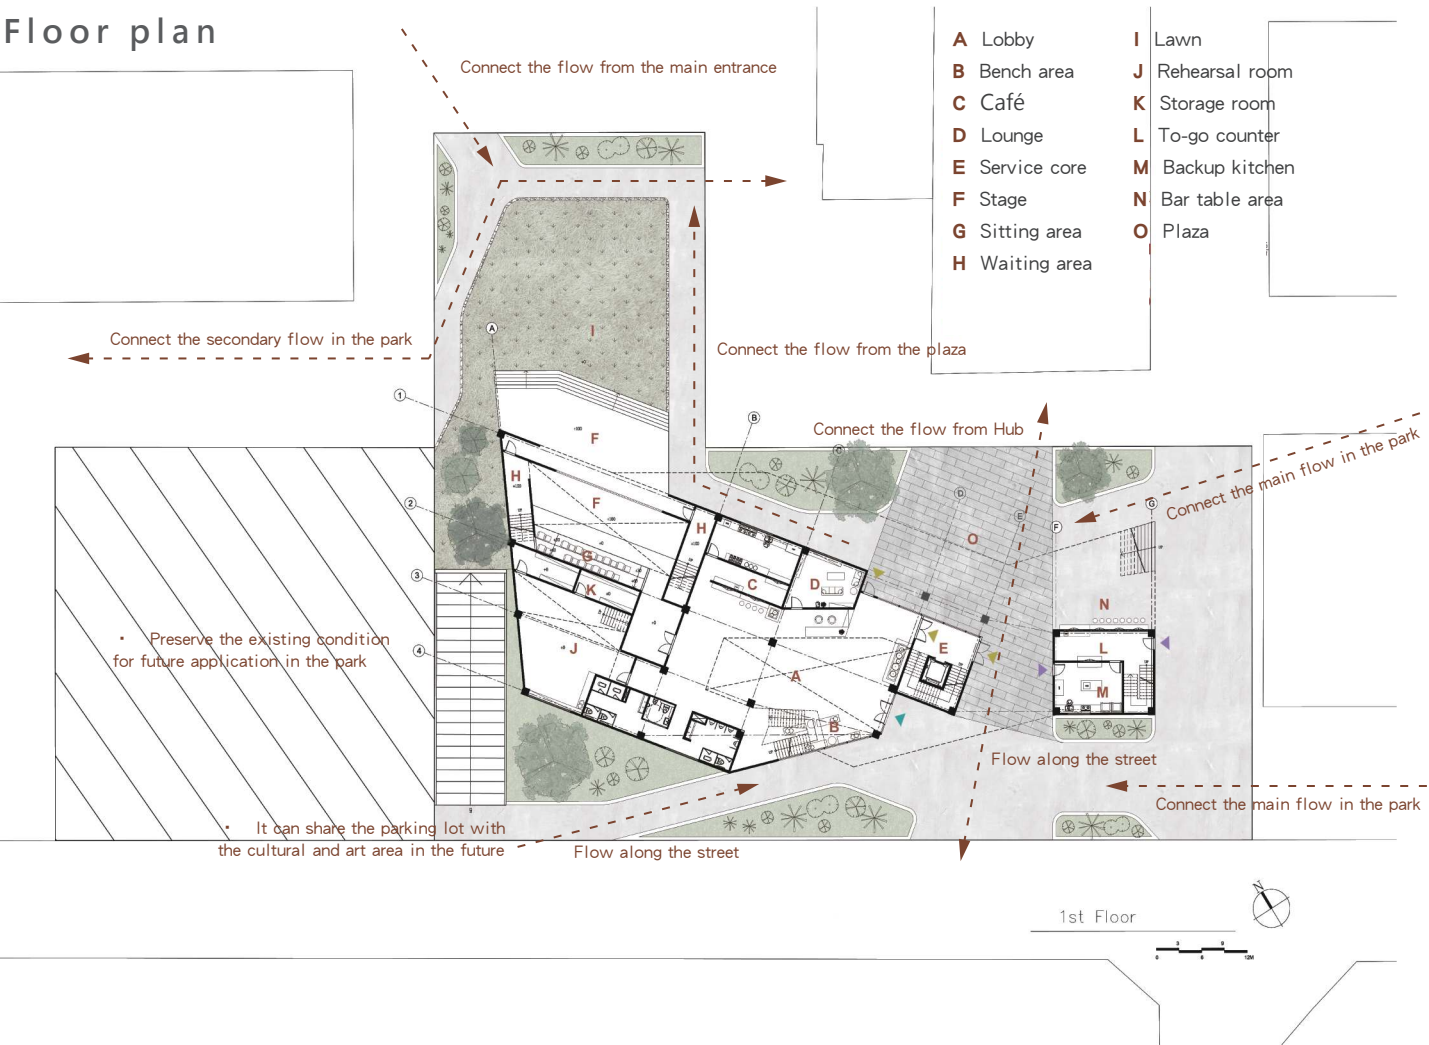





Section

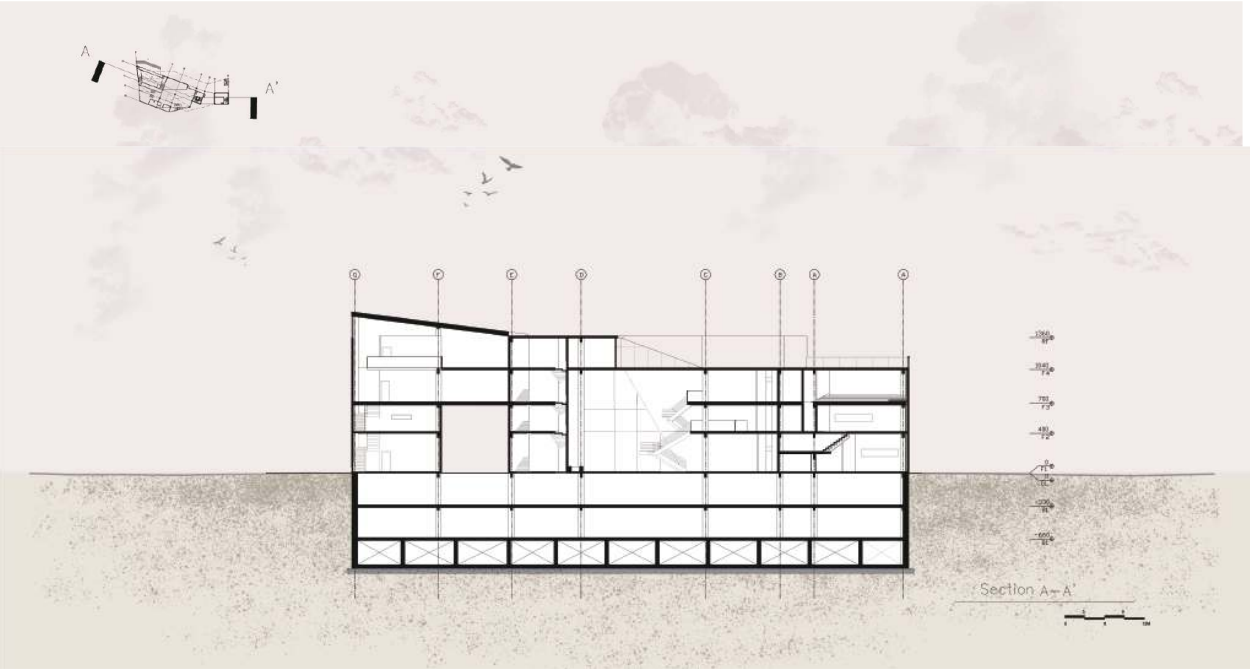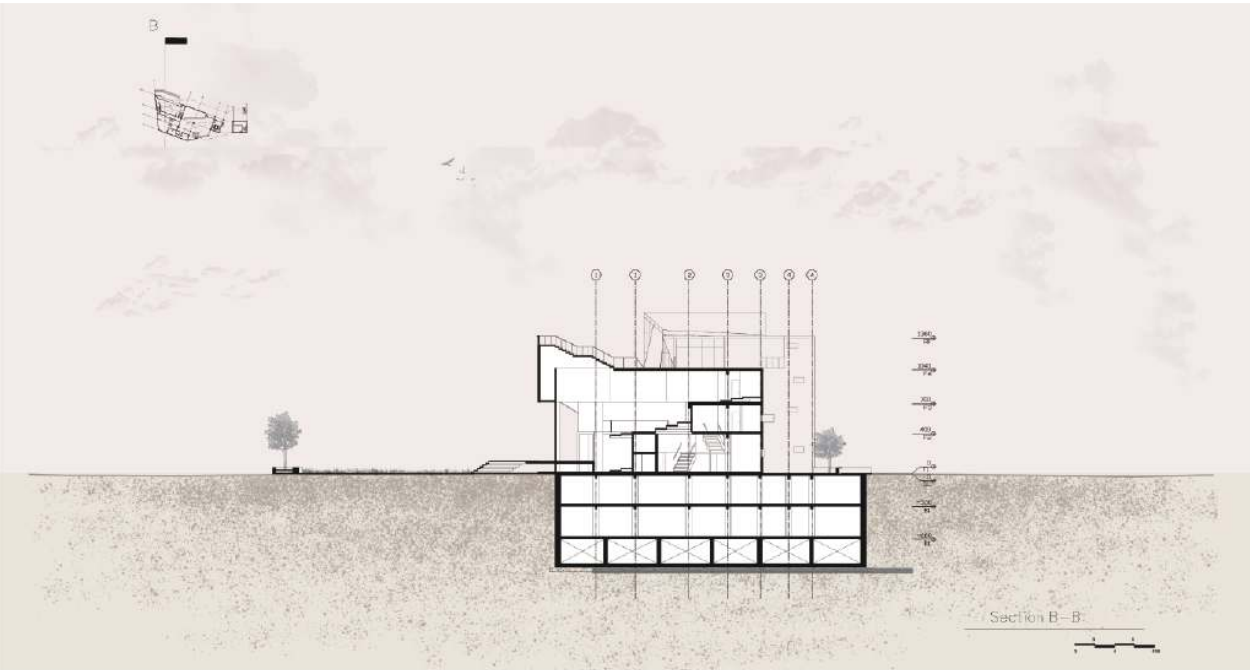

Elevation

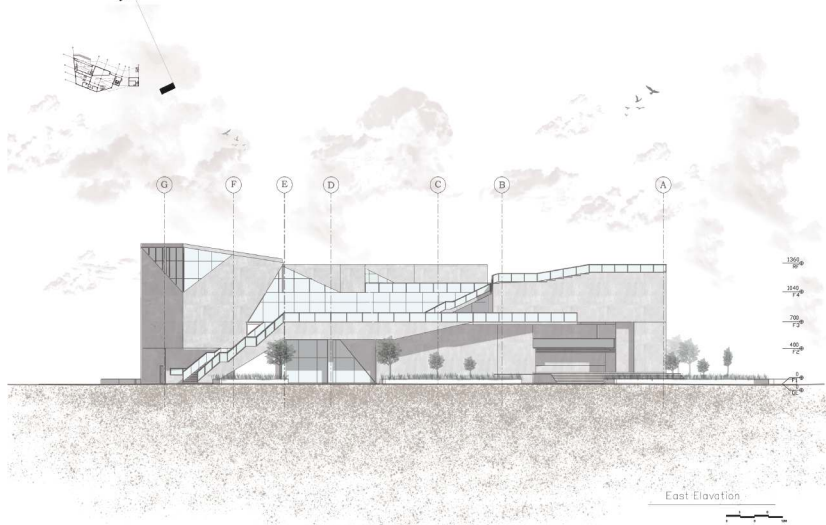

Floor plan

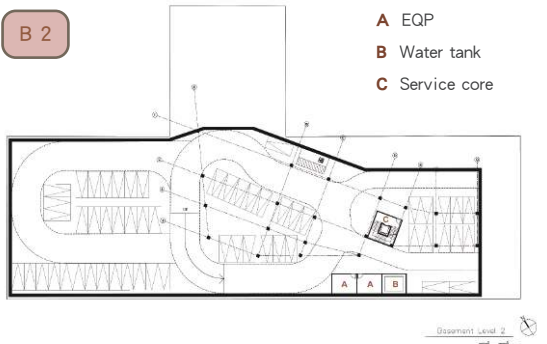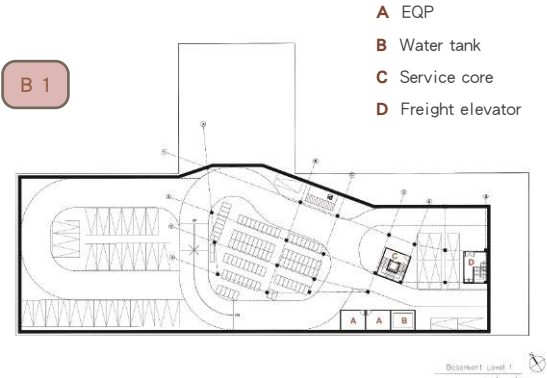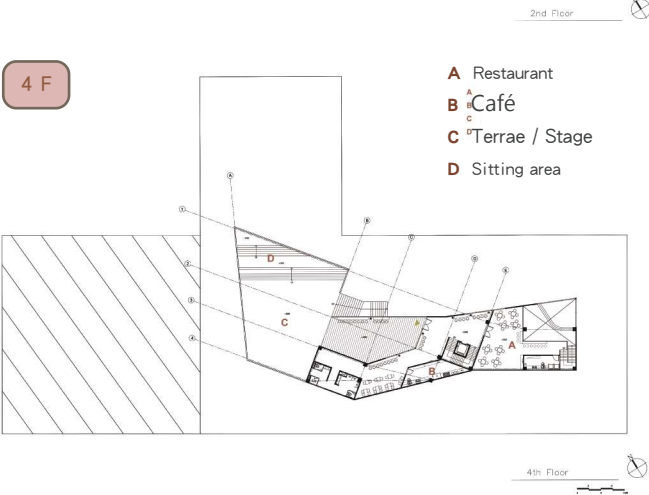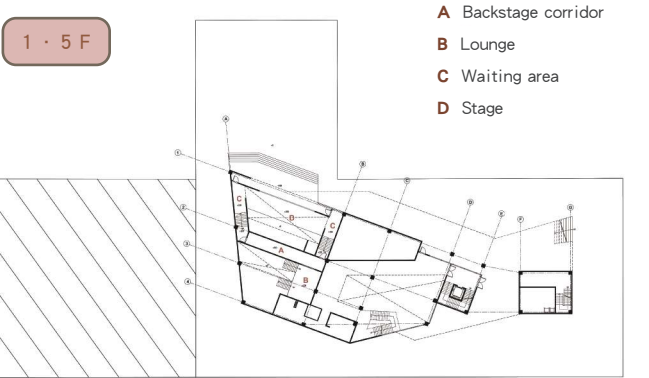

03


Digital Building Fabrication Center

WANDERING

BUT NOT

LOST.

It is believed that natural and the interaction between people may soften the busy atmosphere of traffic or technology. So I got an idea of the bridge which may connect different functions together. As the river flow through the green belt, I want people to wander through the green belt but in a clear and logical way which won't make them get lost. Besides, having a chance to walk out may also become a chance to inspire the thought or slow down the lives.

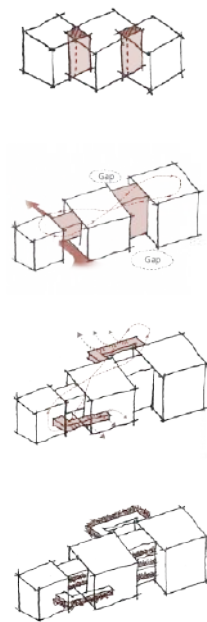


WANDERING

BUT NOT


LOST.




Site plan

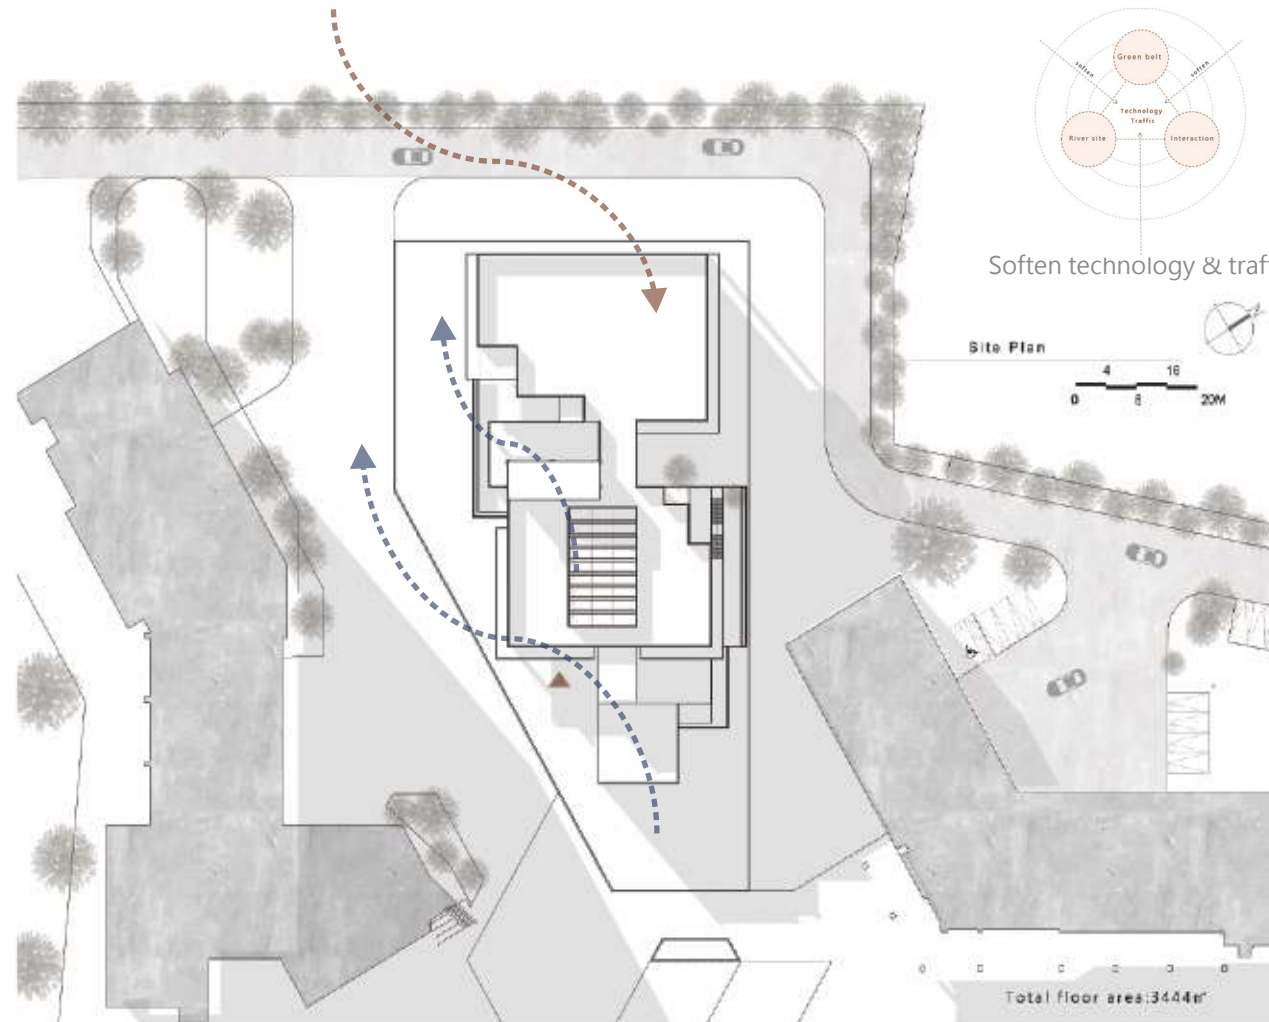


Concept

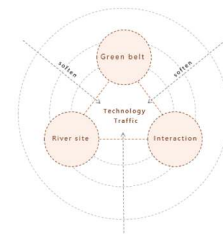


Soften technology & traffic

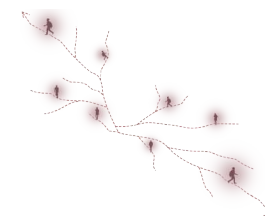

Wandering

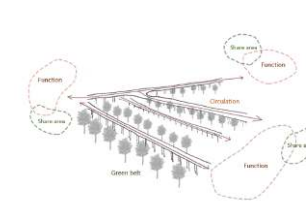


Bridges along with green belt

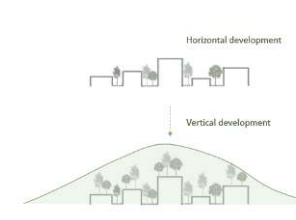


Green belt development

Site analysis



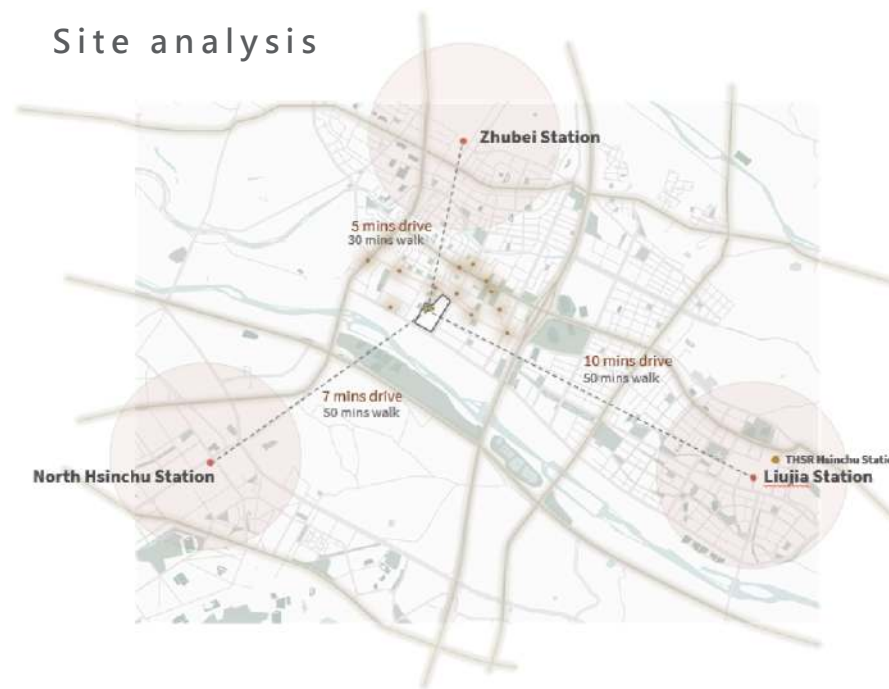


1. ■ Traffic bridge between Hsinchu and Zhubei
■ Connect science and technology institutions
2. ■ Connection between natural and technology
■ Develop into an area for leisure and interaction
3. ■ Railway linking North Hsinchu and Zhubei
4. ■ Way to Industrial Technology Research Institute

- Main road
- Bus stop
- TSHR Hsinchu station
- Train station

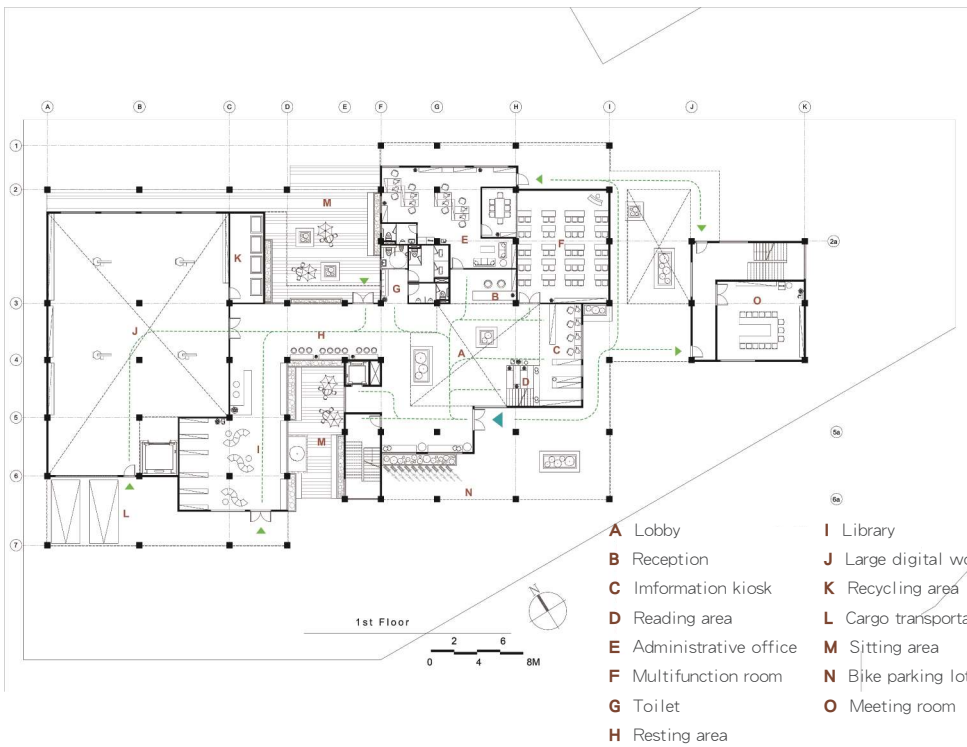

Massing development

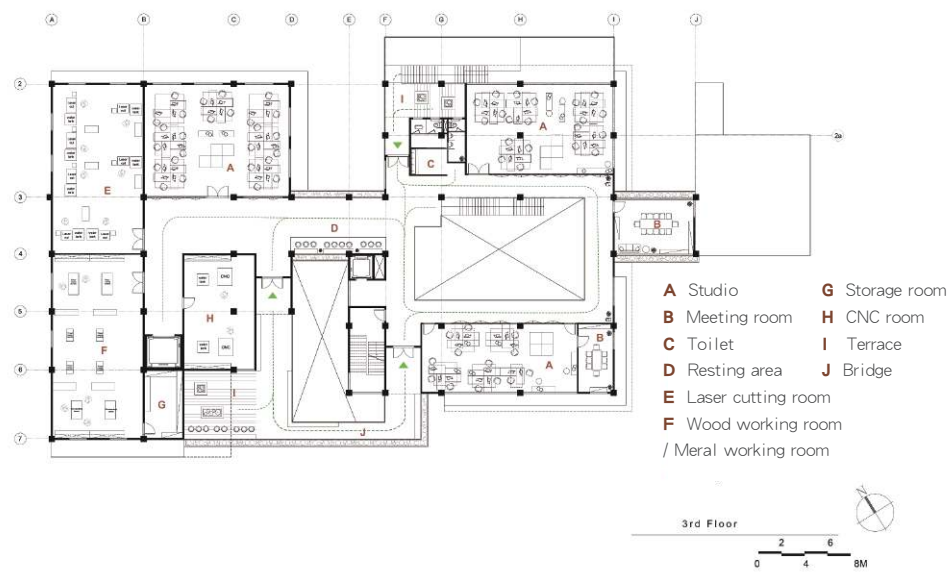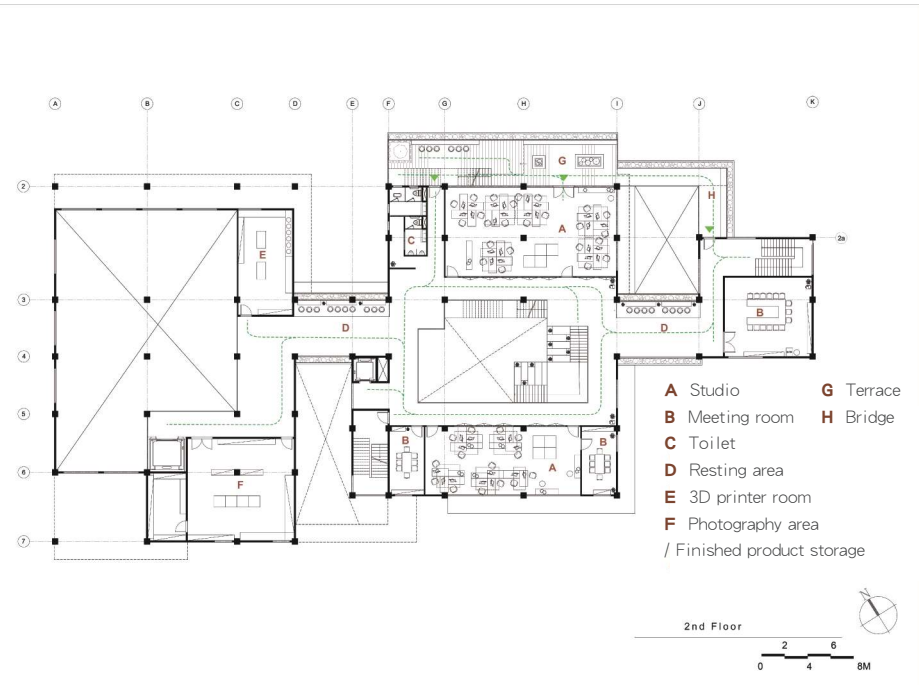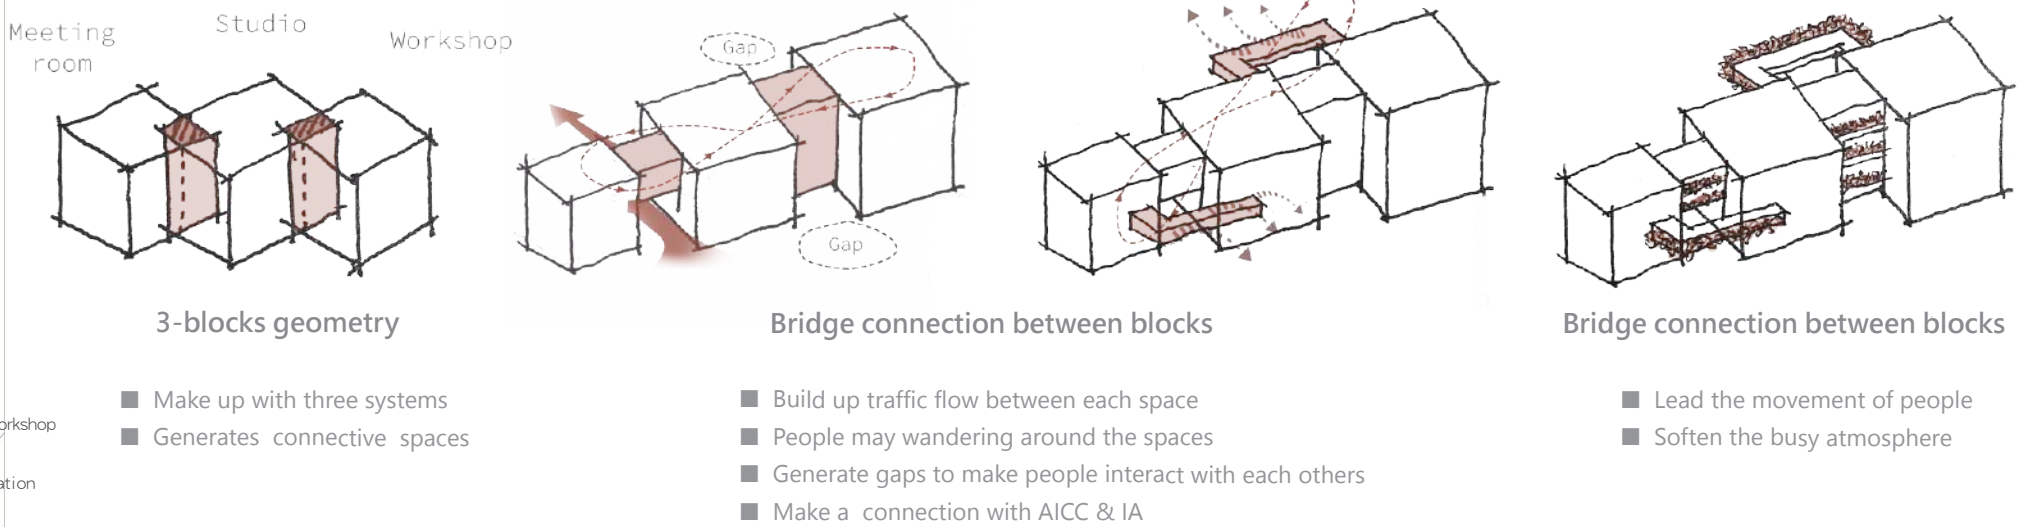

Rendering



Section & Elevation




04

Hydrological Exhibition Center

In this design, the site will be defined as an exhibition center closely linked to "hydrology." Located between the the "river" and "lake," the site becomes a transitional space between the two, using the interactions with water to form classification and variation, and provides a space for the public to experience the ecosystem deeply. Also, the river system will be brought into the site along with the traffic flow, creating an interconnected water space between the indoor and outdoor areas. Additionally, it shapes a central water plaza and a water stage to gather people and leverage the landscape advantages to interact with the river and lake. Eventually, we hope to strengthen the connection between people and hydrology within this space, as well as to raise awareness of the significance of the hydrological ecology in this site, combining landscape, performance, and water to evoke a unique resonance.




伴
水之間

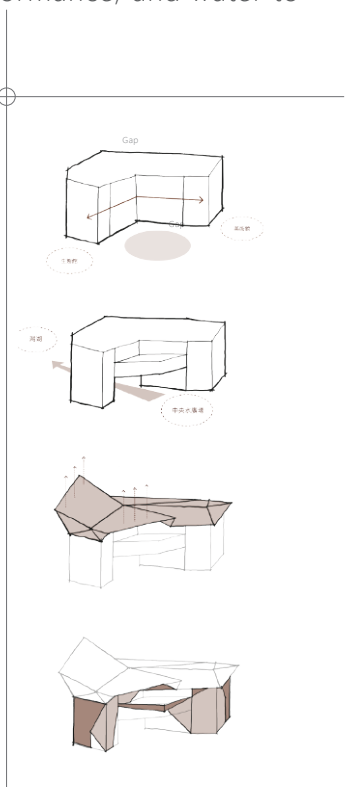

Massing



Concept

Function

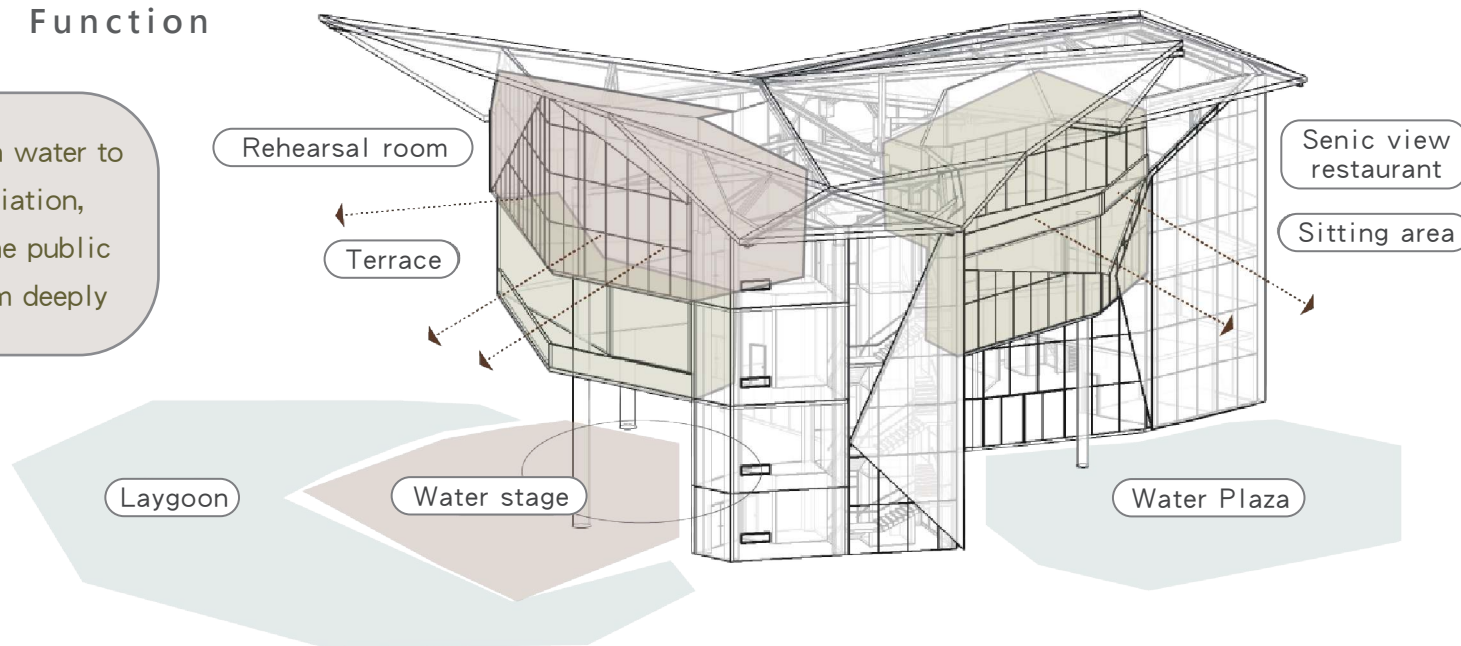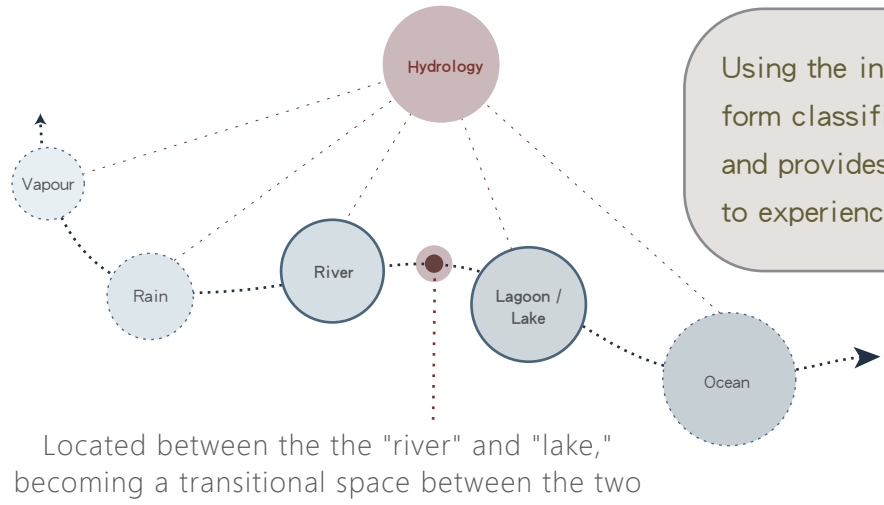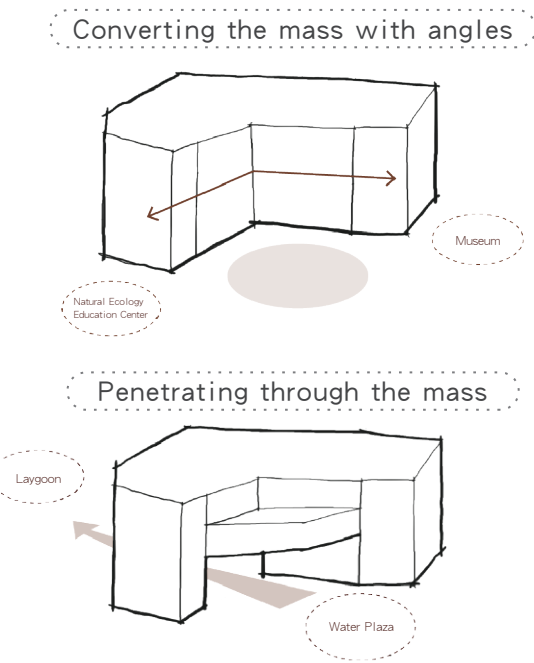

About X space

Floor Plan - 1F

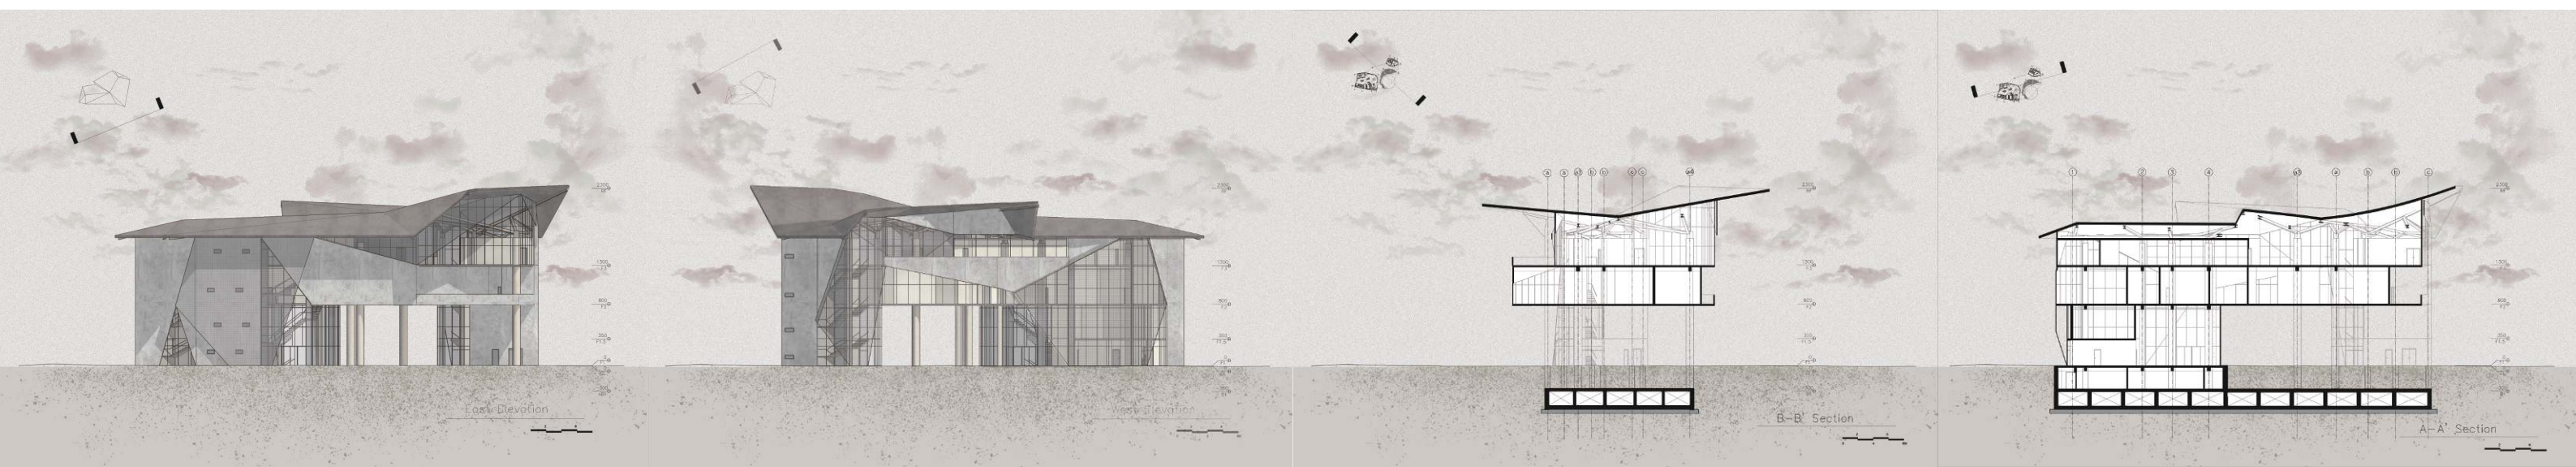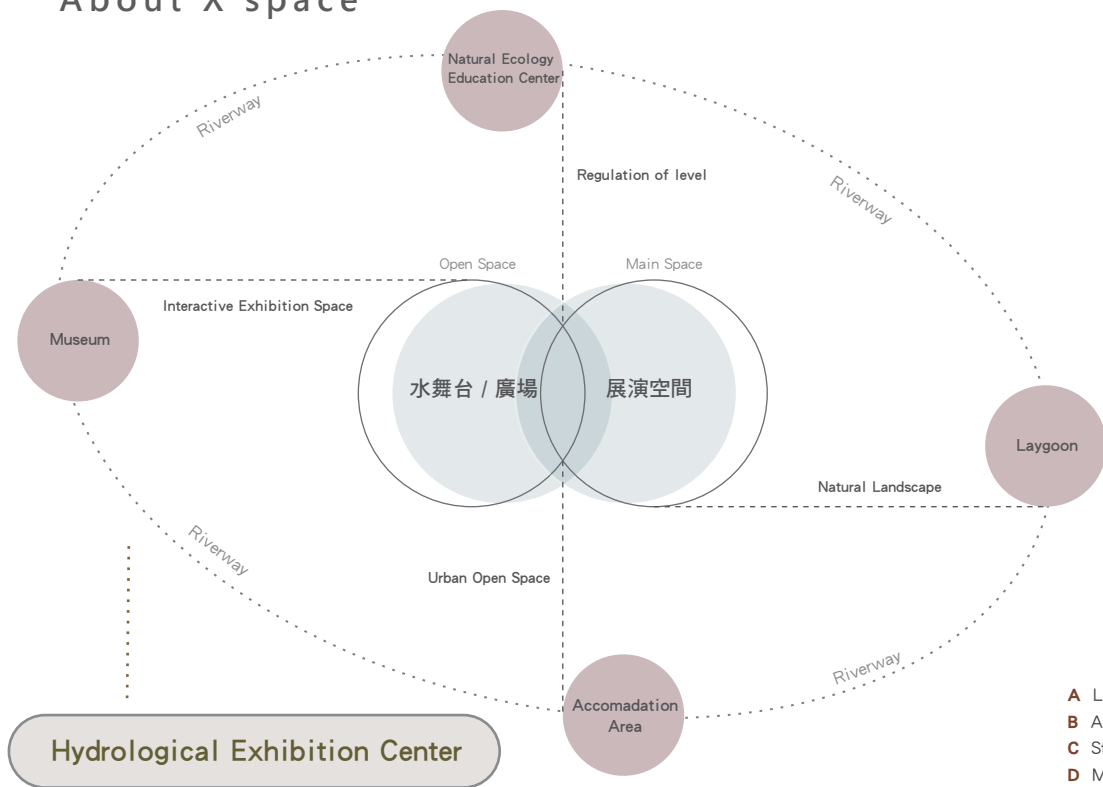

Hydrology Exhibition Center

Milk board, kraft liner, chipboard,
grid paper, acrylic pmma,
wood stick, iron wire,
scouring pad


Scale: 1/200



Youth hostel model

Milk board, kraft liner,
grid paper,
wood stick, iron wire,
scouring pad




Scale: 1/100

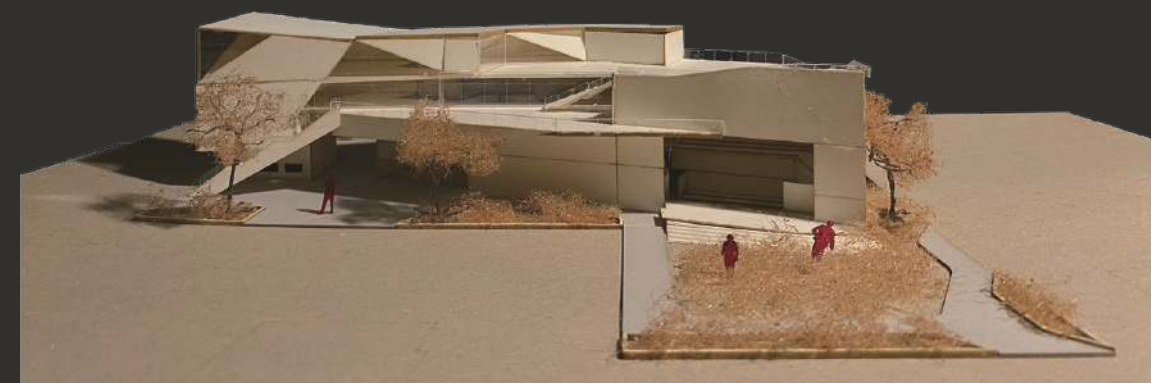

Dinner theater model

Milk board, chip board,
clear water cardboard,
acrylic pmma,
iron wire,
scouring pad

Scale: 1/200

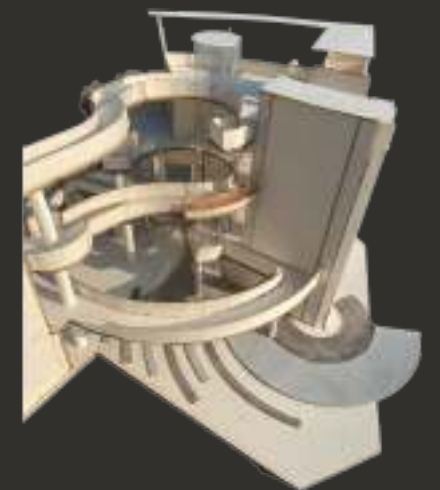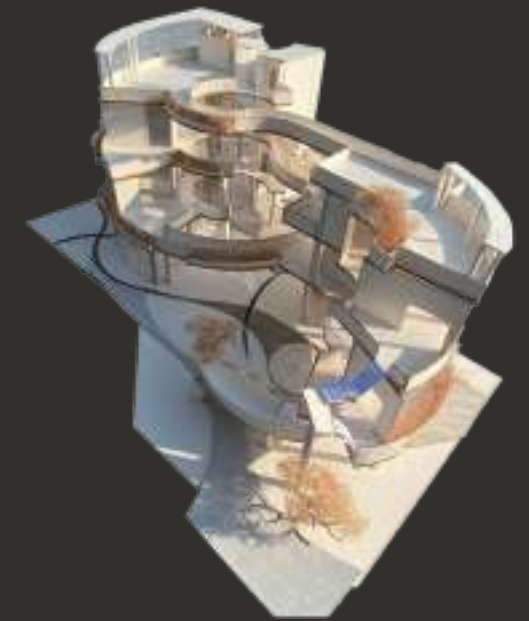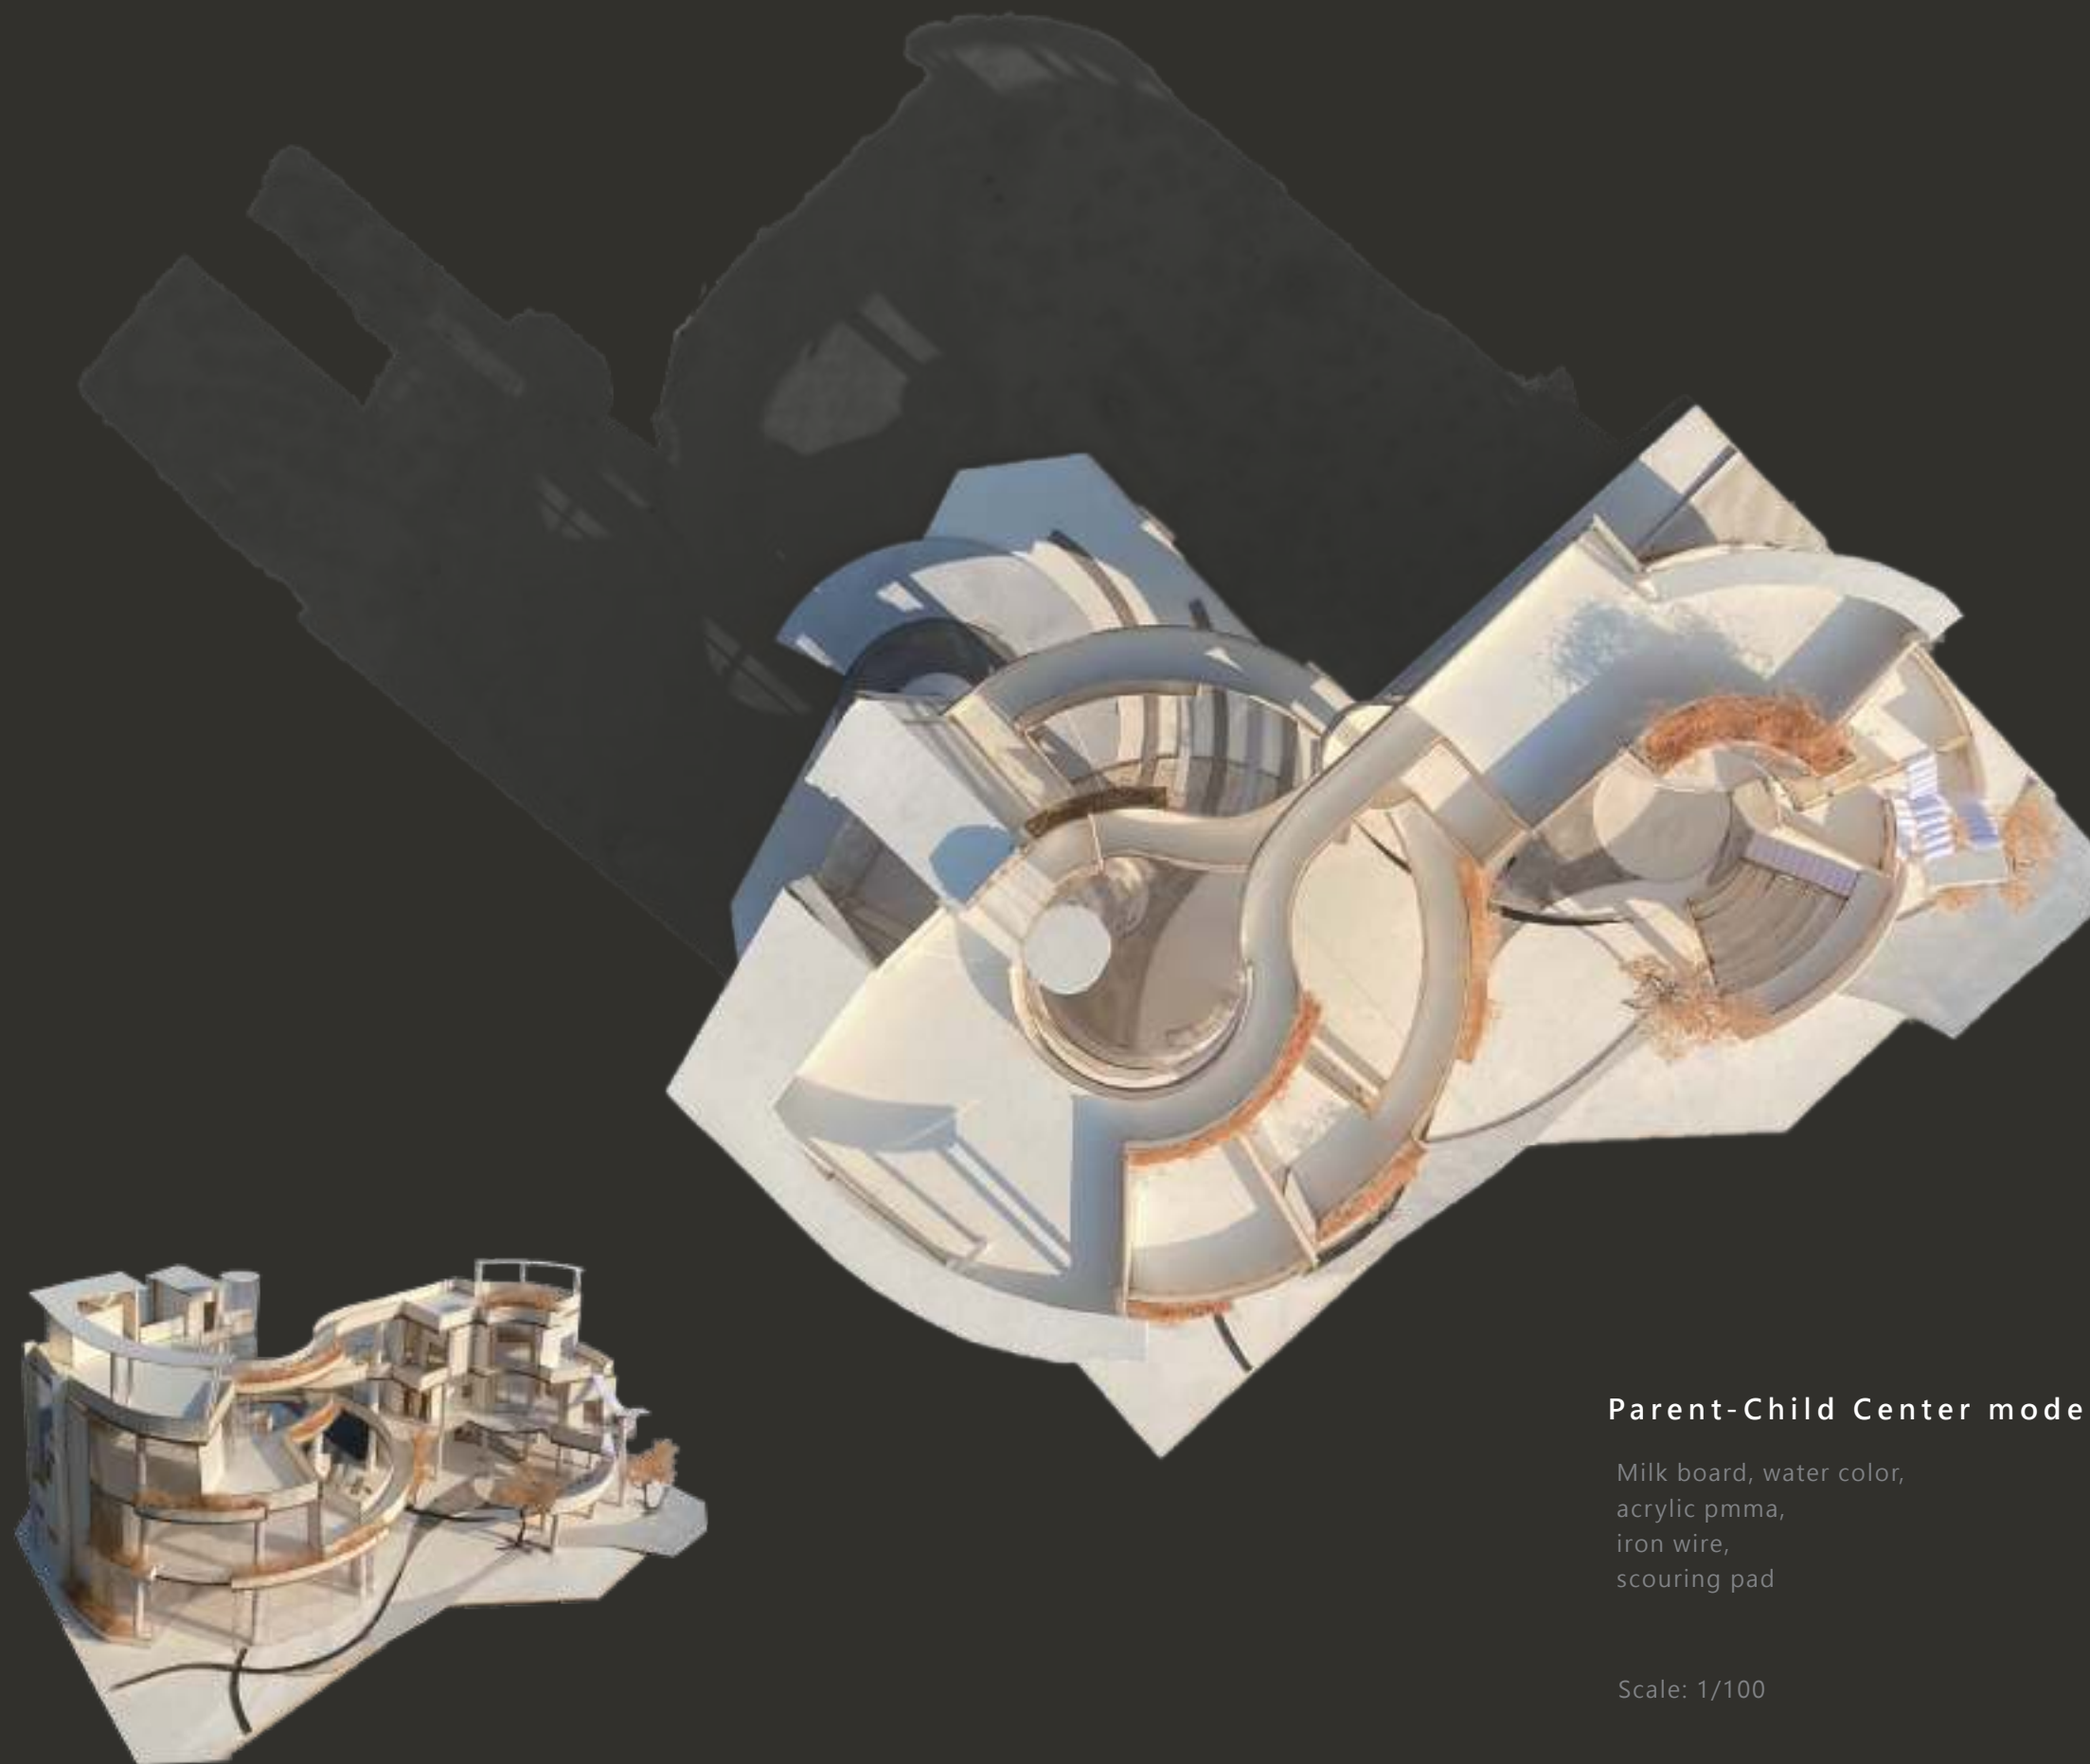

Parent-Child Center model

Milk board, water color,
acrylic pmma,
iron wire,
scouring pad

Scale: 1/100

Sketching

